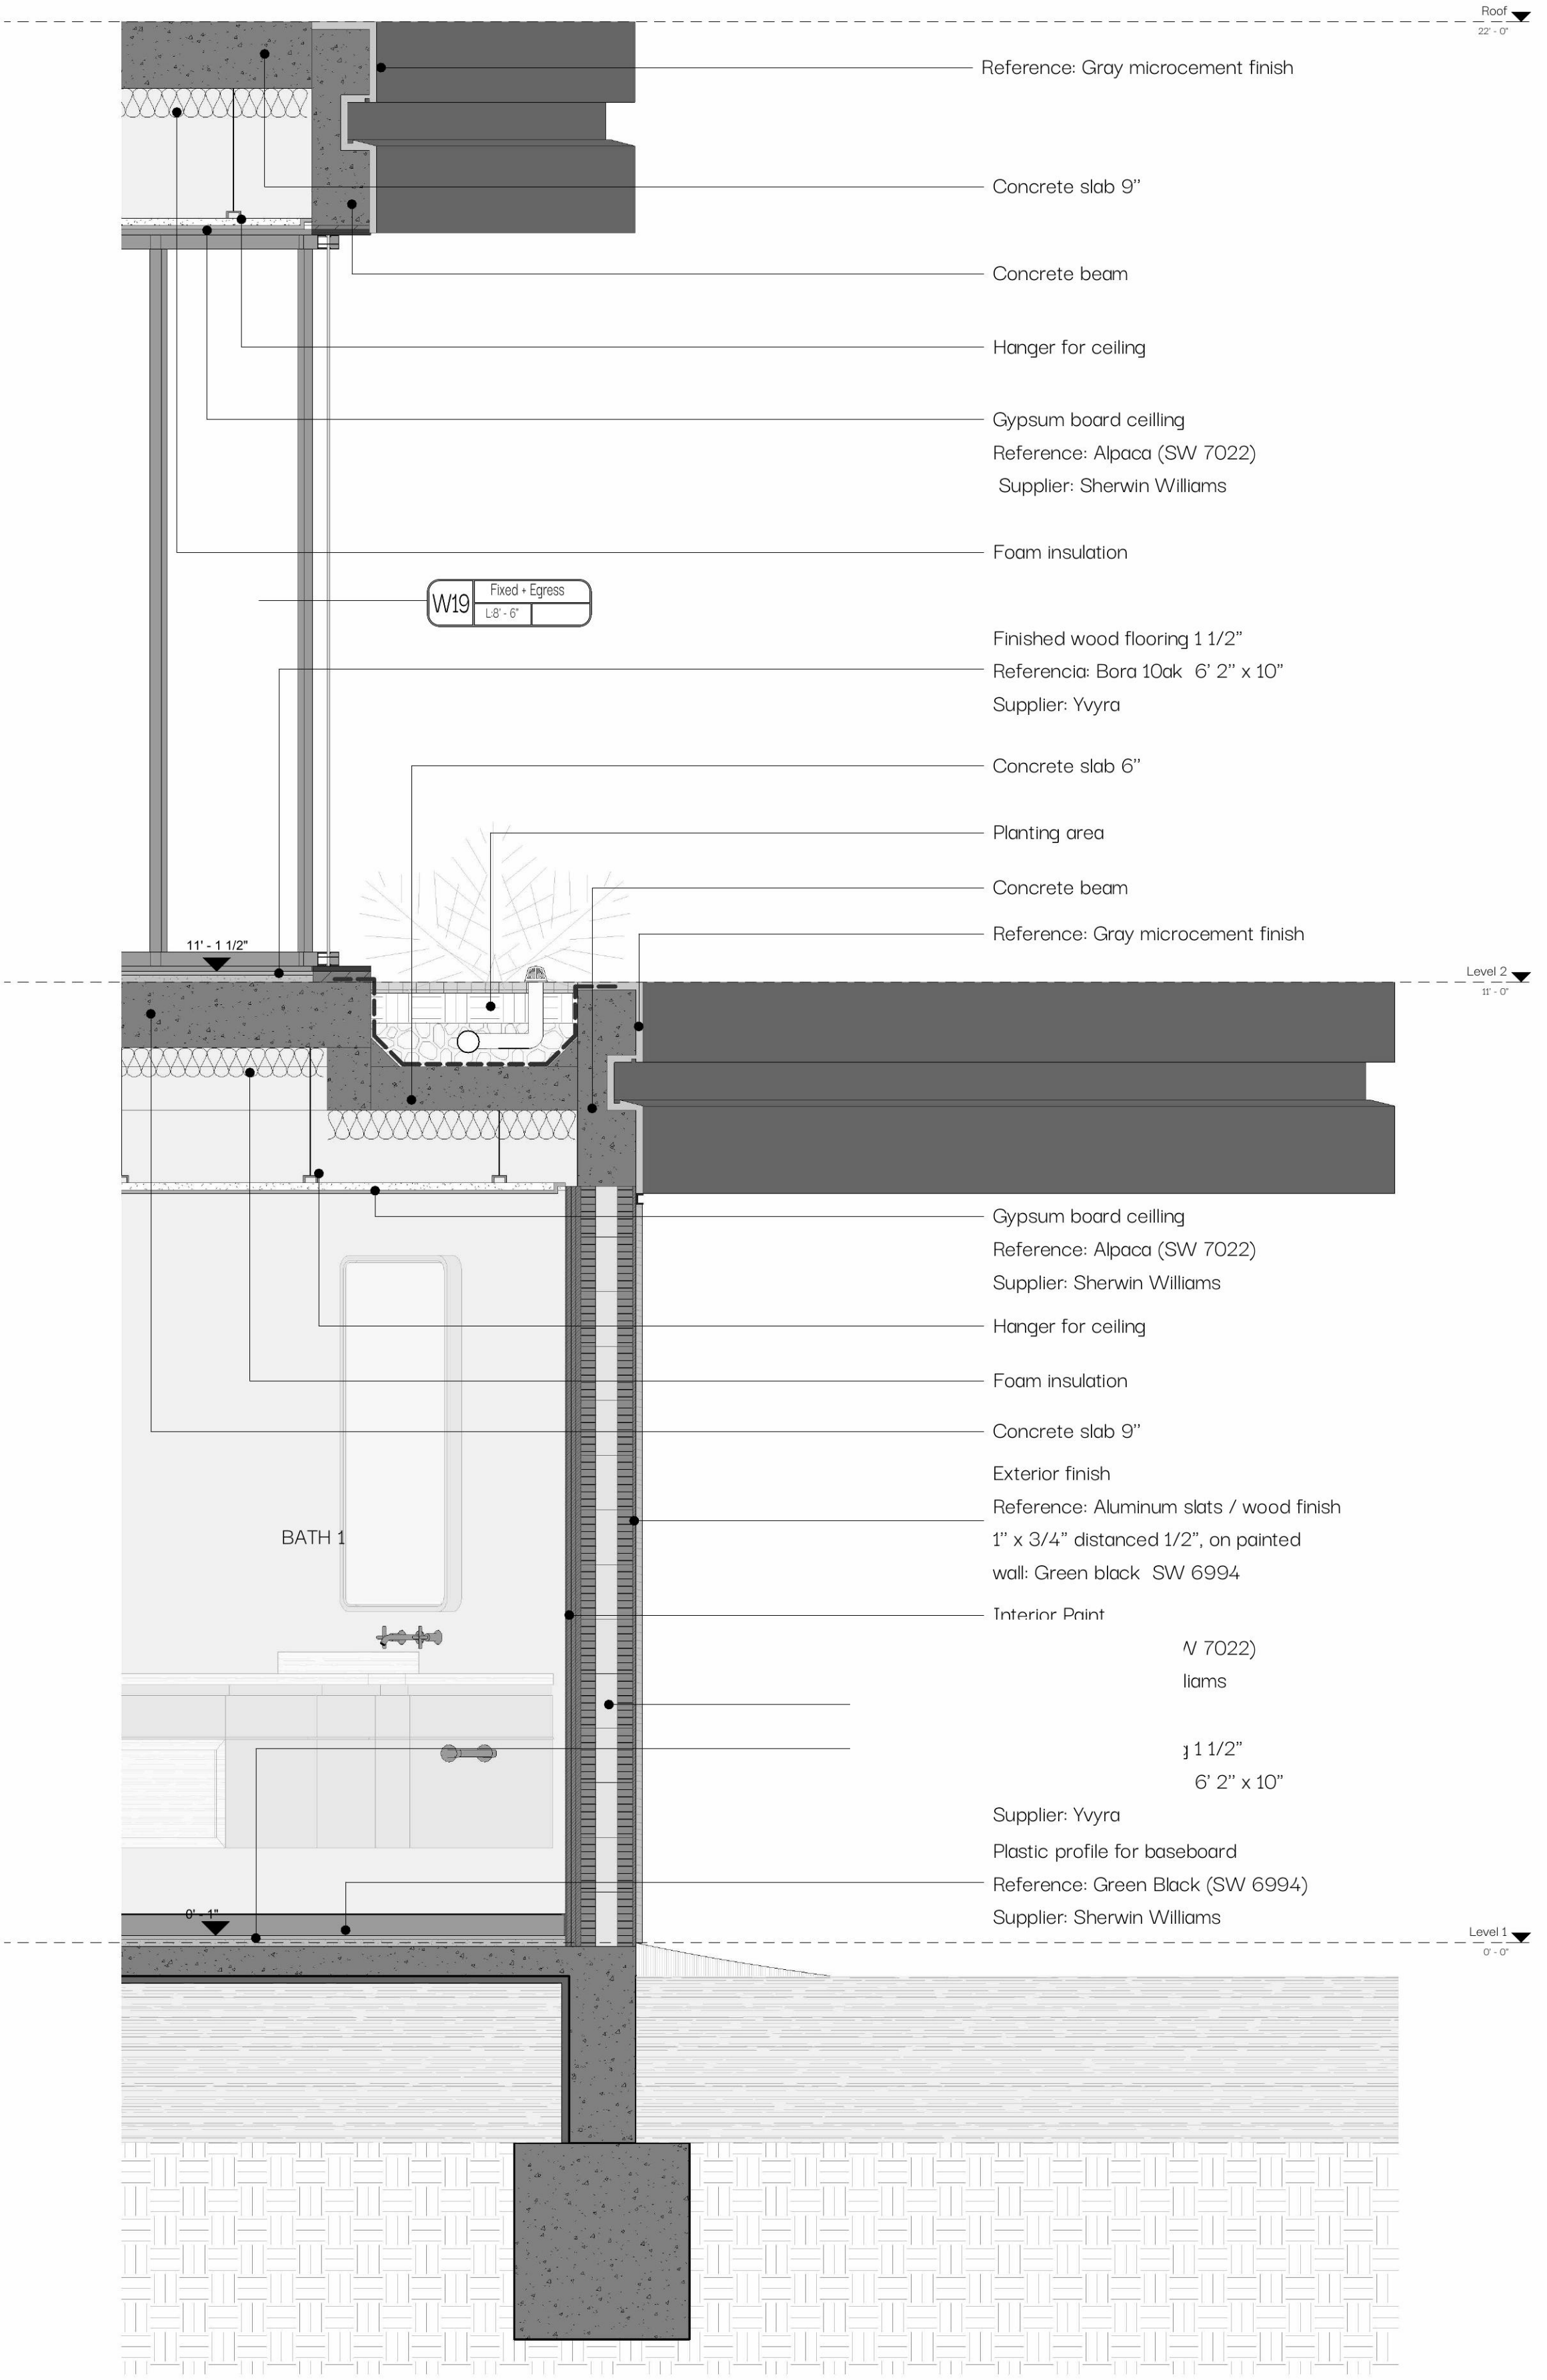

Roof
22' - 0"
Reference: Gray microcement finish
Concrete slab 9"
Concrete beam
Hanger for ceiling
Gypsum board ceilling
Reference: Alpaca (SW 7022)
Supplier: Sherwin Williams
Foam insulation
W19
Fixed + Egress
L:8' - 6"
Finished wood flooring 1 1/2"
Referencia: Bora 10ak 6' 2" x 10"
Supplier: Yvyra
Concrete slab 6"
Planting area
Concrete beam
Reference: Gray microcement finish
11' - 1 1/2"
Level 2
11' - 0"
Gypsum board ceilling
Reference: Alpaca (SW 7022)
Supplier: Sherwin Williams
Hanger for ceiling
Foam insulation
Concrete slab 9"
Exterior finish
Reference: Aluminum slats / wood finish
1" x 3/4" distanced 1/2", on painted
wall: Green black SW 6994
Interior Paint
N 7022)
liams
g 1 1/2"
6' 2" x 10"
Supplier: Yvyra
Plastic profile for baseboard
Reference: Green Black (SW 6994)
Supplier: Sherwin Williams
BATH 1
0' - 1"
Level 1
0' - 0"