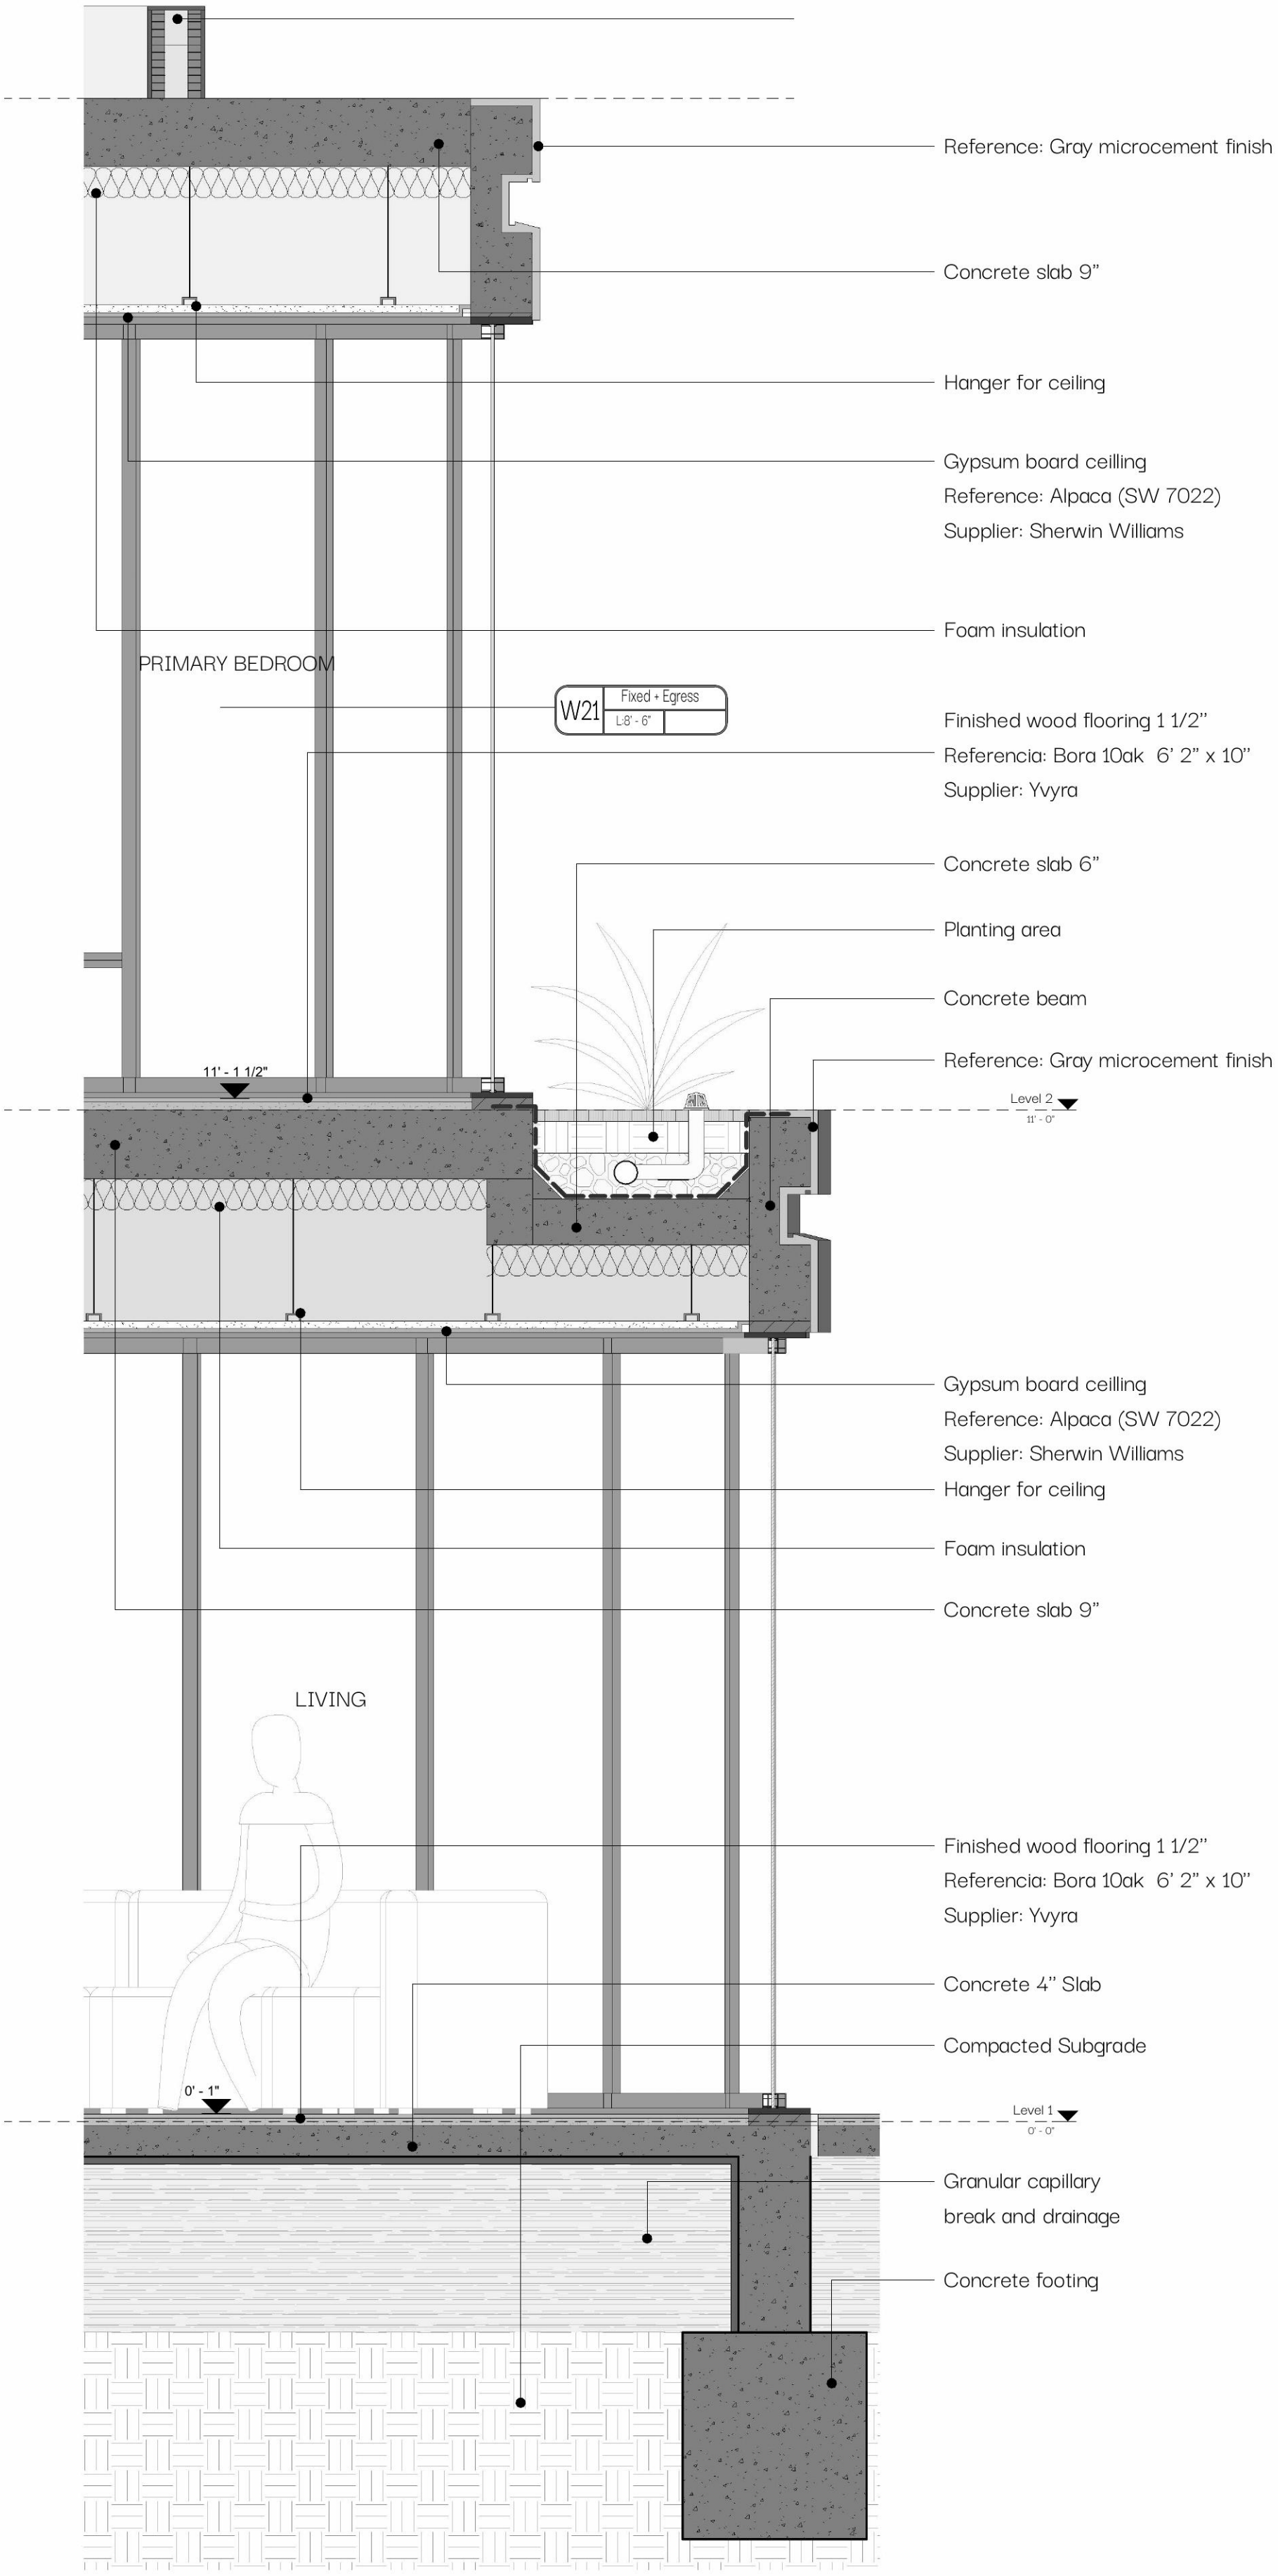

Reference: Gray microcement finish
Concrete slab 9”
Hanger for ceiling
Gypsum board ceilling
Reference: Alpaca (SW 7022)
Supplier: Sherwin Williams
Foam insulation
PRIMARY BEDROOM
W21
Fixed + Egress
L:8' - 6"
Finished wood flooring 1 1/2”
Referencia: Bora 10ak 6’ 2” x 10”
Supplier: Yvyra
Concrete slab 6”
Planting area
Concrete beam
Reference: Gray microcement finish
11' - 1 1/2"
Level 2
11' - 0"
Gypsum board ceilling
Reference: Alpaca (SW 7022)
Supplier: Sherwin Williams
Hanger for ceiling
Foam insulation
Concrete slab 9”
LIVING
Finished wood flooring 1 1/2”
Referencia: Bora 10ak 6’ 2” x 10”
Supplier: Yvyra
Concrete 4” Slab
Compacted Subgrade
0' - 1"
Level 1
0' - 0"
Granular capillary
break and drainage
Concrete footing