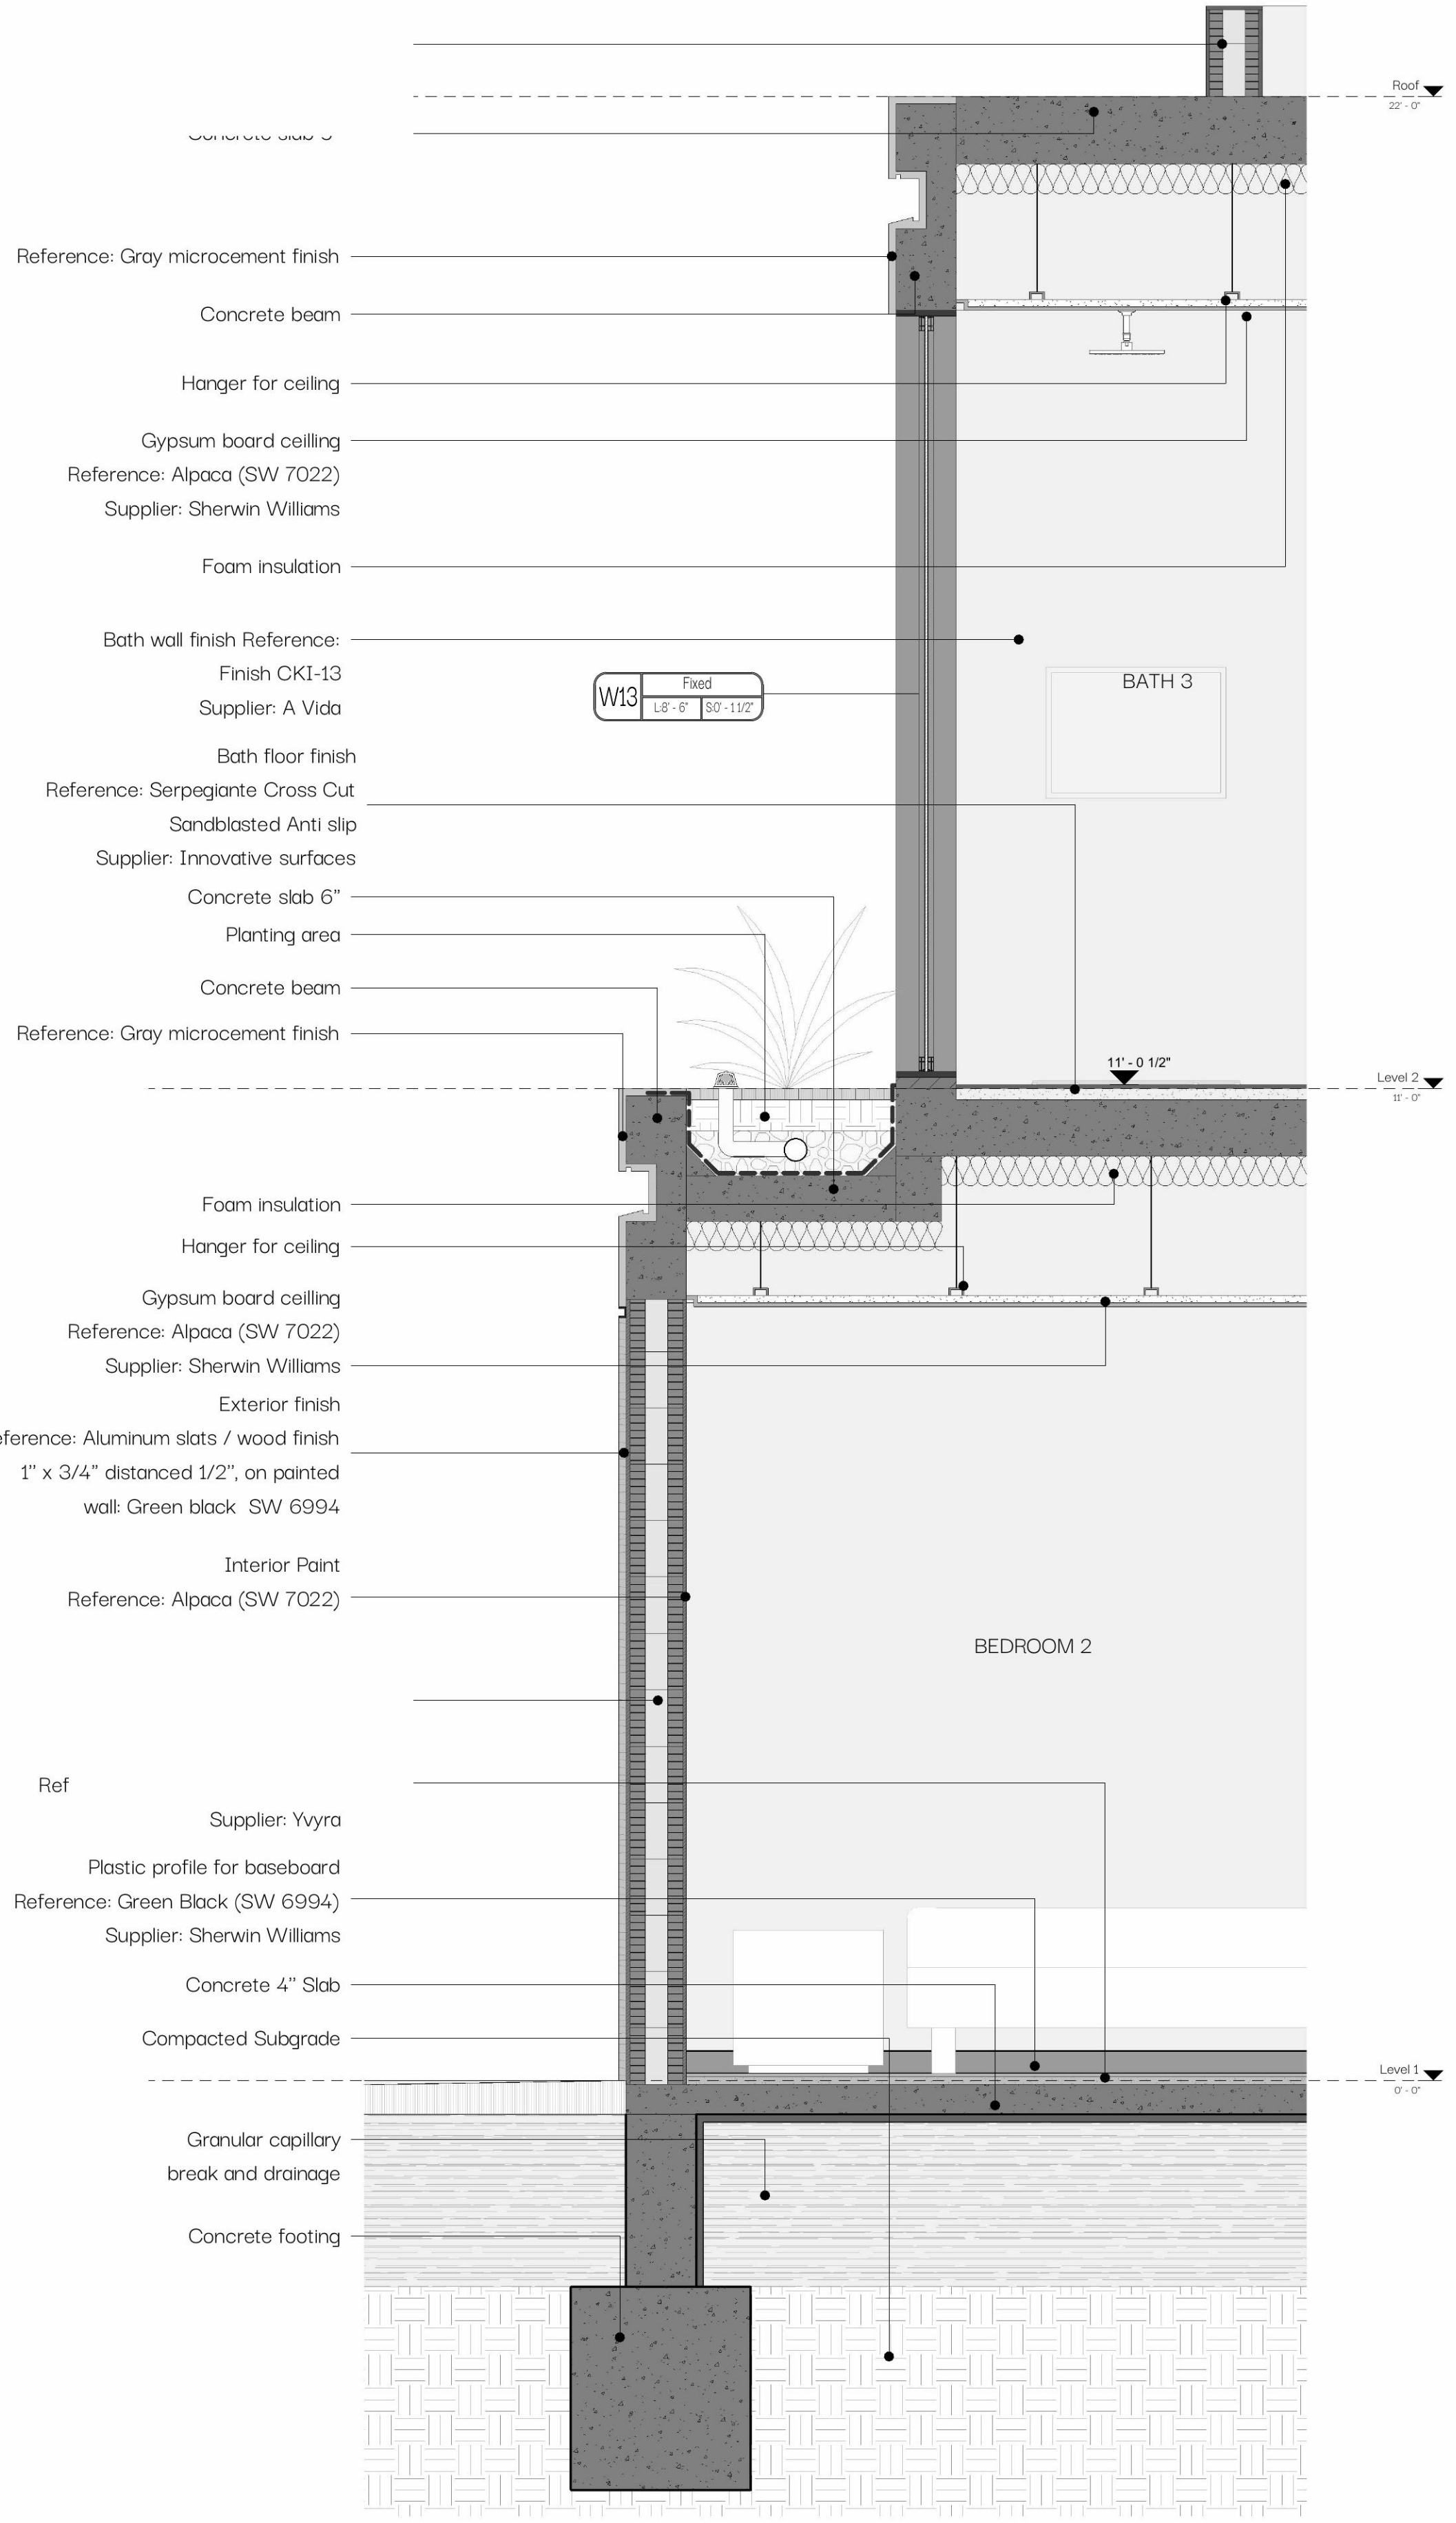

Roof
22' - 0"
Reference: Gray microcement finish
Concrete beam
Hanger for ceiling
Gypsum board ceilling
Reference: Alpaca (SW 7022)
Supplier: Sherwin Williams
Foam insulation
Bath wall finish Reference:
Finish CKI-13
Supplier: A Vida
W13
Fixed
L:8' - 6"
S:0' - 11/2"
BATH 3
Bath floor finish
Reference: Serpegiante Cross Cut
Sandblasted Anti slip
Supplier: Innovative surfaces
Concrete slab 6”
Planting area
Concrete beam
Reference: Gray microcement finish
11' - 0 1/2"
Level 2
11' - 0"
Foam insulation
Hanger for ceiling
Gypsum board ceilling
Reference: Alpaca (SW 7022)
Supplier: Sherwin Williams
Exterior finish
Reference: Aluminum slats / wood finish
1” x 3/4” distanced 1/2”, on painted
wall: Green black SW 6994
Interior Paint
Reference: Alpaca (SW 7022)
BEDROOM 2
Ref
Supplier: Yvyra
Plastic profile for baseboard
Reference: Green Black (SW 6994)
Supplier: Sherwin Williams
Concrete 4” Slab
Compacted Subgrade
Level 1
0' - 0"
Granular capillary
break and drainage
Concrete footing