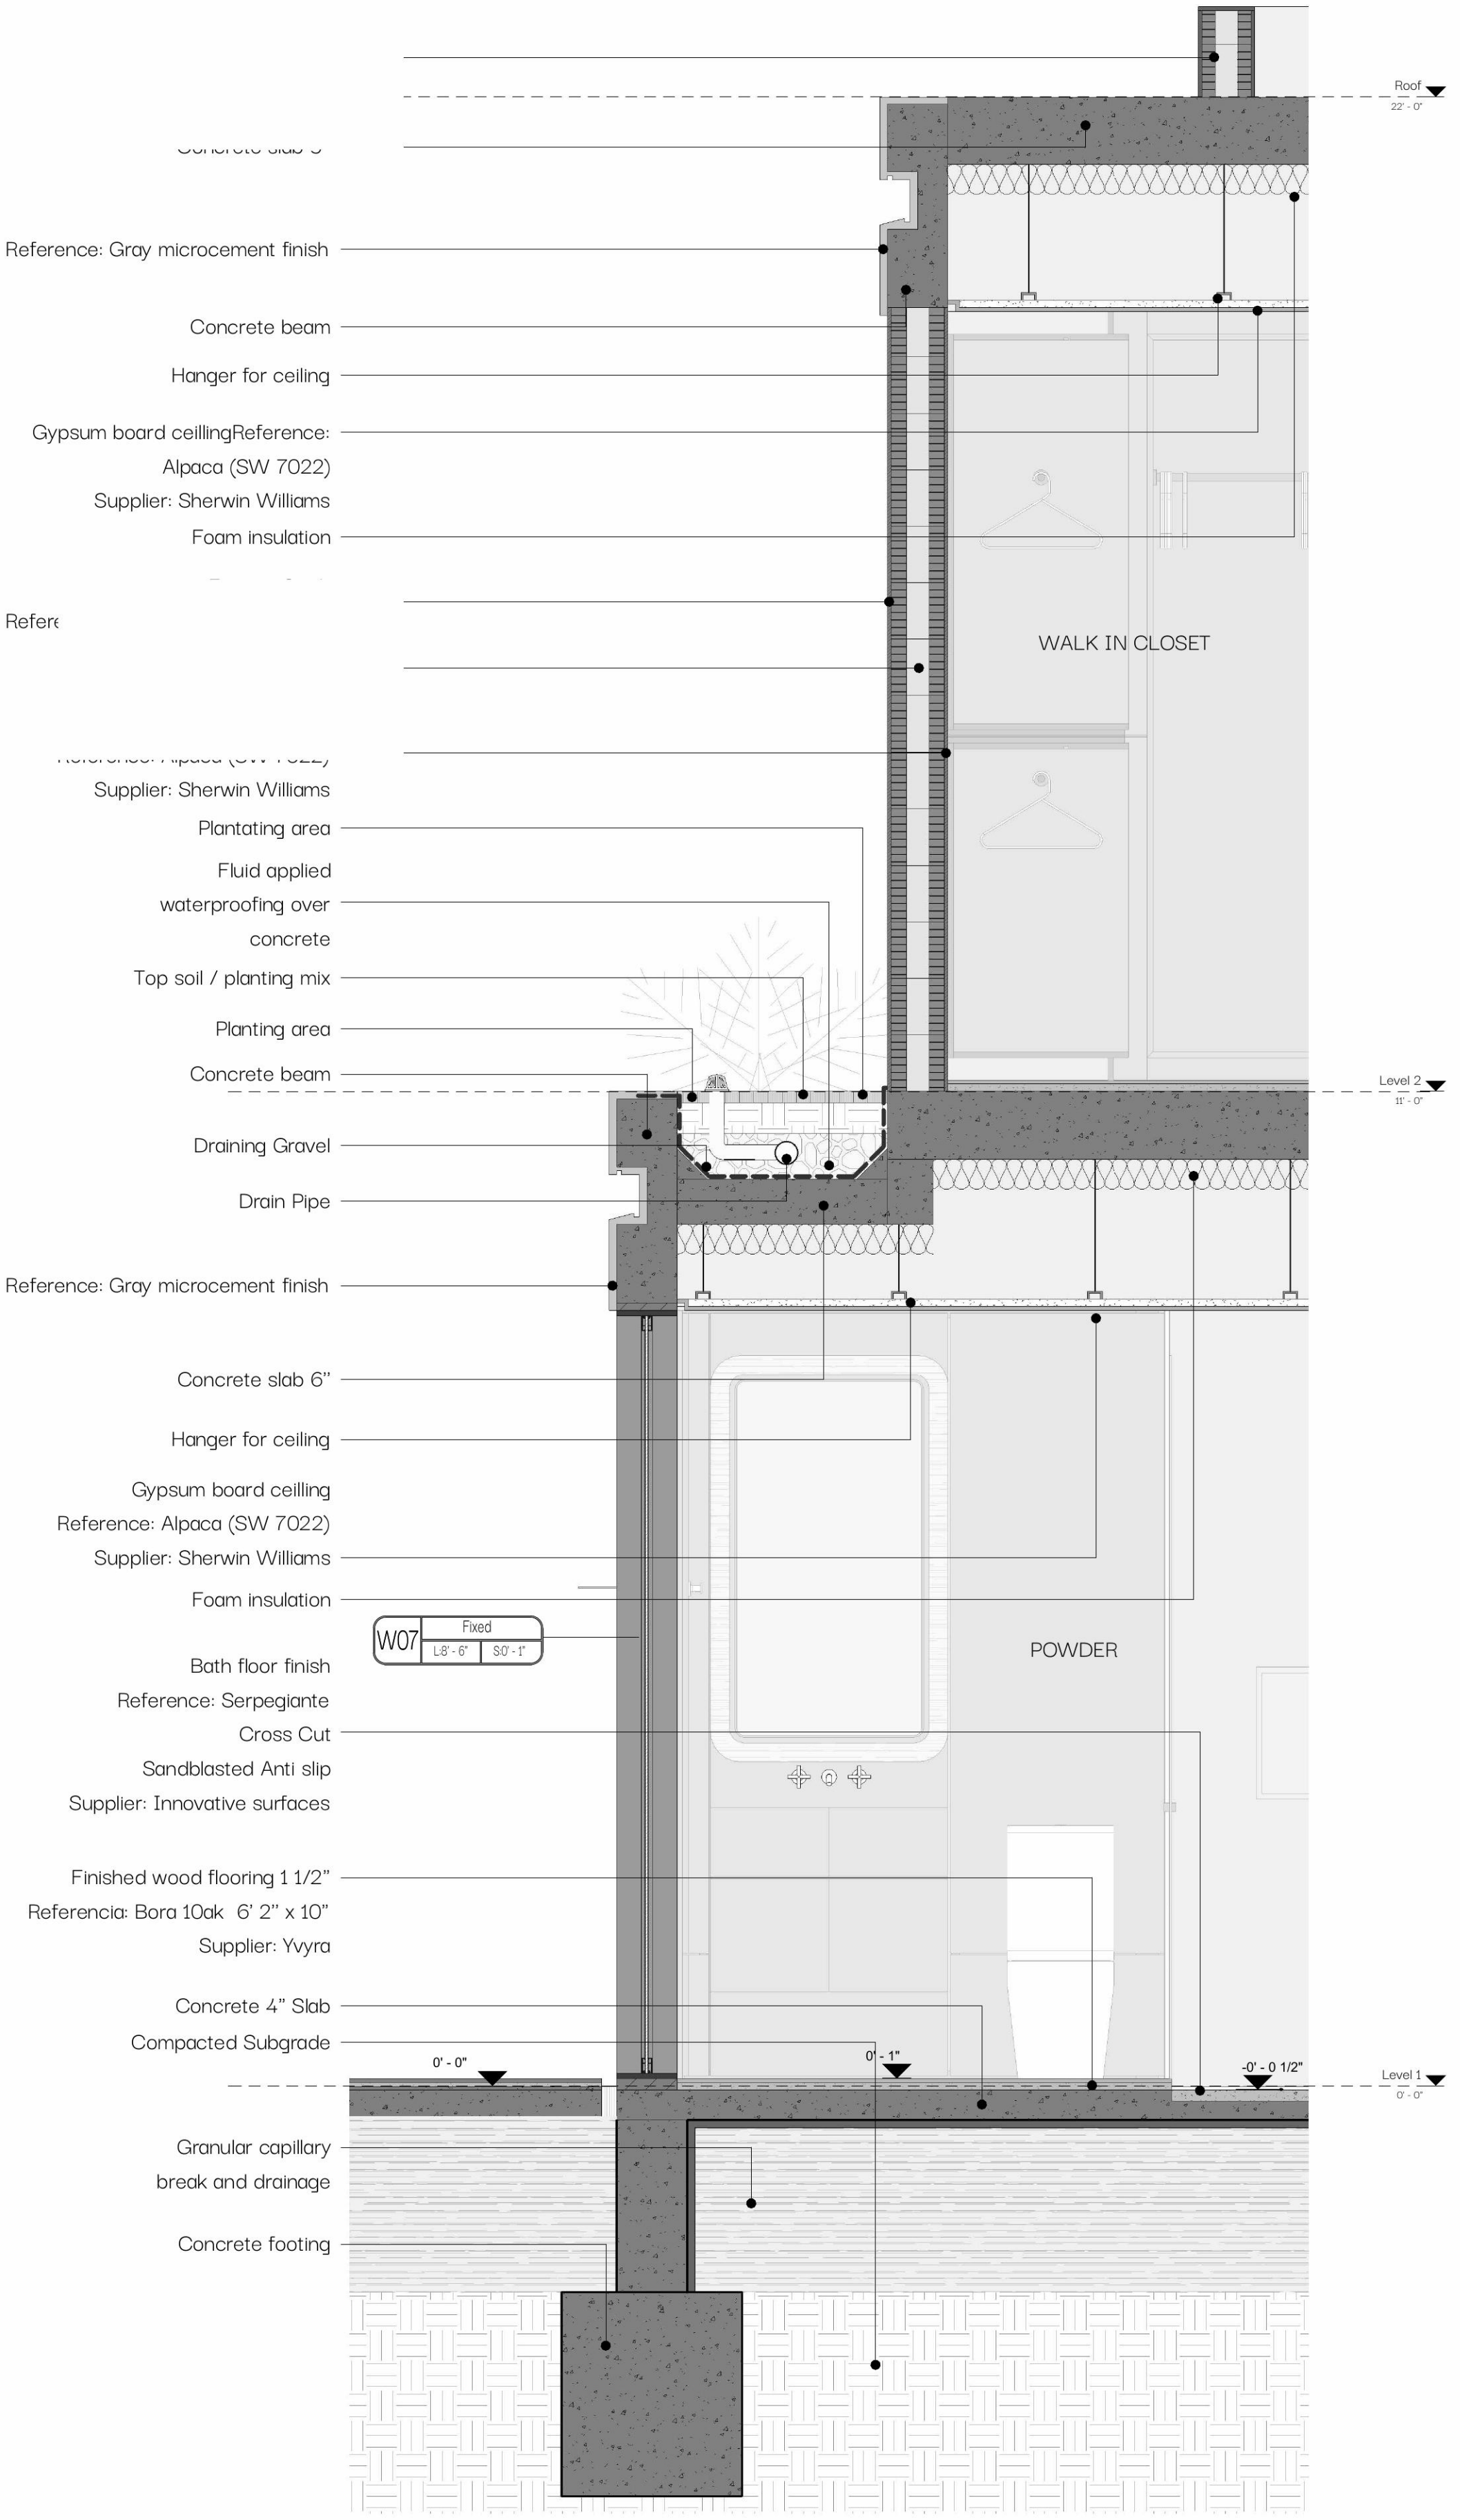

Roof
22' - 0"
Reference: Gray microcement finish
Concrete beam
Hanger for ceiling
Gypsum board ceillingReference:
Alpaca (SW 7022)
Supplier: Sherwin Williams
Foam insulation
Supplier: Sherwin Williams
Plantating area
Fluid applied
waterproofing over
concrete
Top soil / planting mix
Planting area
Concrete beam
Draining Gravel
Drain Pipe
Reference: Gray microcement finish
Concrete slab 6"
Hanger for ceiling
Gypsum board ceilling
Reference: Alpaca (SW 7022)
Supplier: Sherwin Williams
Foam insulation
W07
Fixed
L:8' - 6"
S:0' - 1"
Bath floor finish
Reference: Serpegiante
Cross Cut
Sandblasted Anti slip
Supplier: Innovative surfaces
Finished wood flooring 1 1/2"
Referencia: Bora 10ak 6' 2" x 10"
Supplier: Yvyra
Concrete 4" Slab
Compacted Subgrade
Granular capillary
break and drainage
Concrete footing
WALK IN CLOSET
POWDER
Level 2
11' - 0"
0' - 0"
0' - 1"
-0' - 0 1/2"
Level 1
0' - 0"